
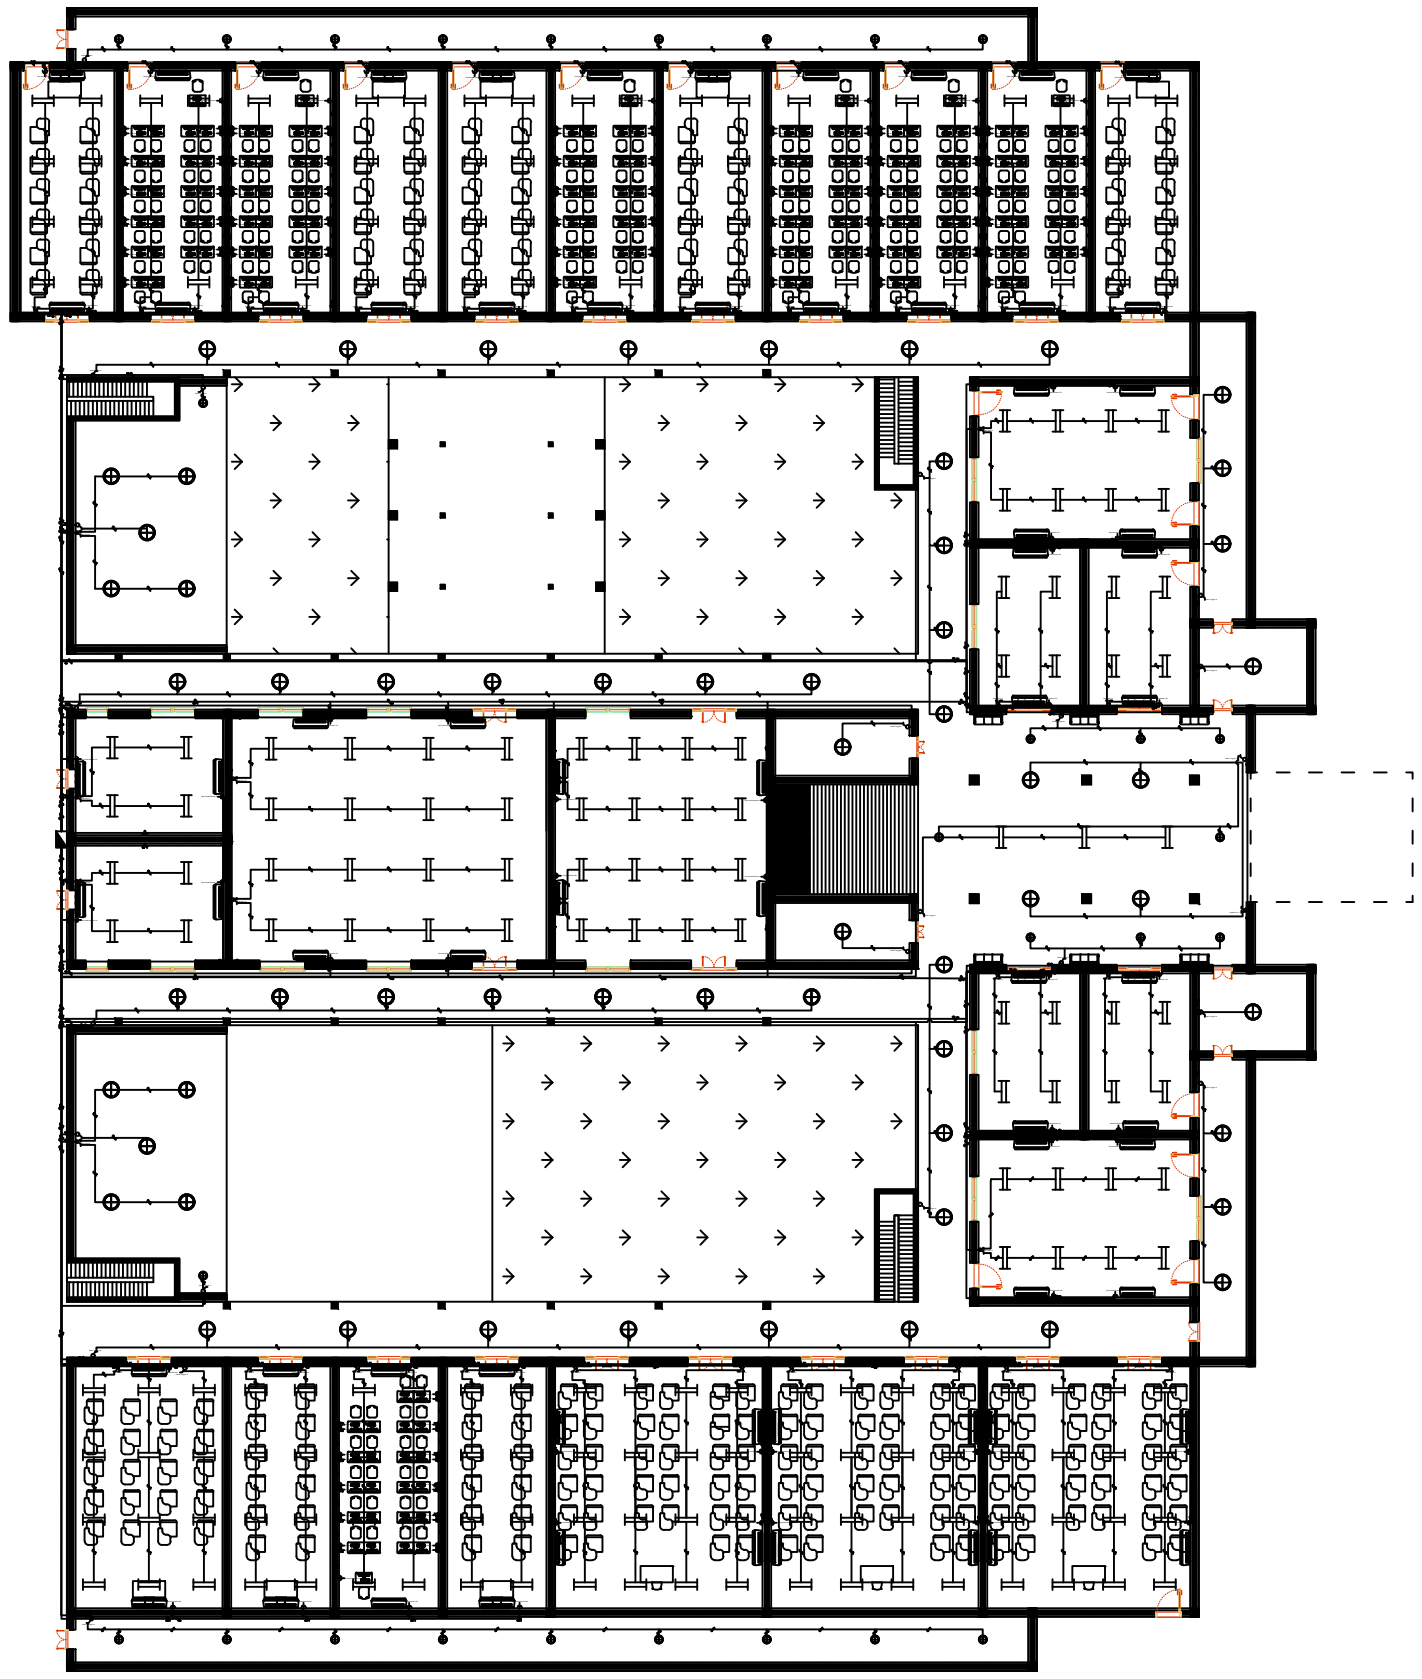


Project SLD Instalasi Listrik Gedung Herman Yohannes Lantai 1		Tanggal	24 Oktober 2024
		Digambar	Farrel Amaris Ipaenen Mirza Dyiaulhaq
		Dicek	Romy Dzaki Zharfan Hisyam Rifa'i Ma'ruf
Satuan: cm	Skala: 1:350	Ukuran Kertas	A3

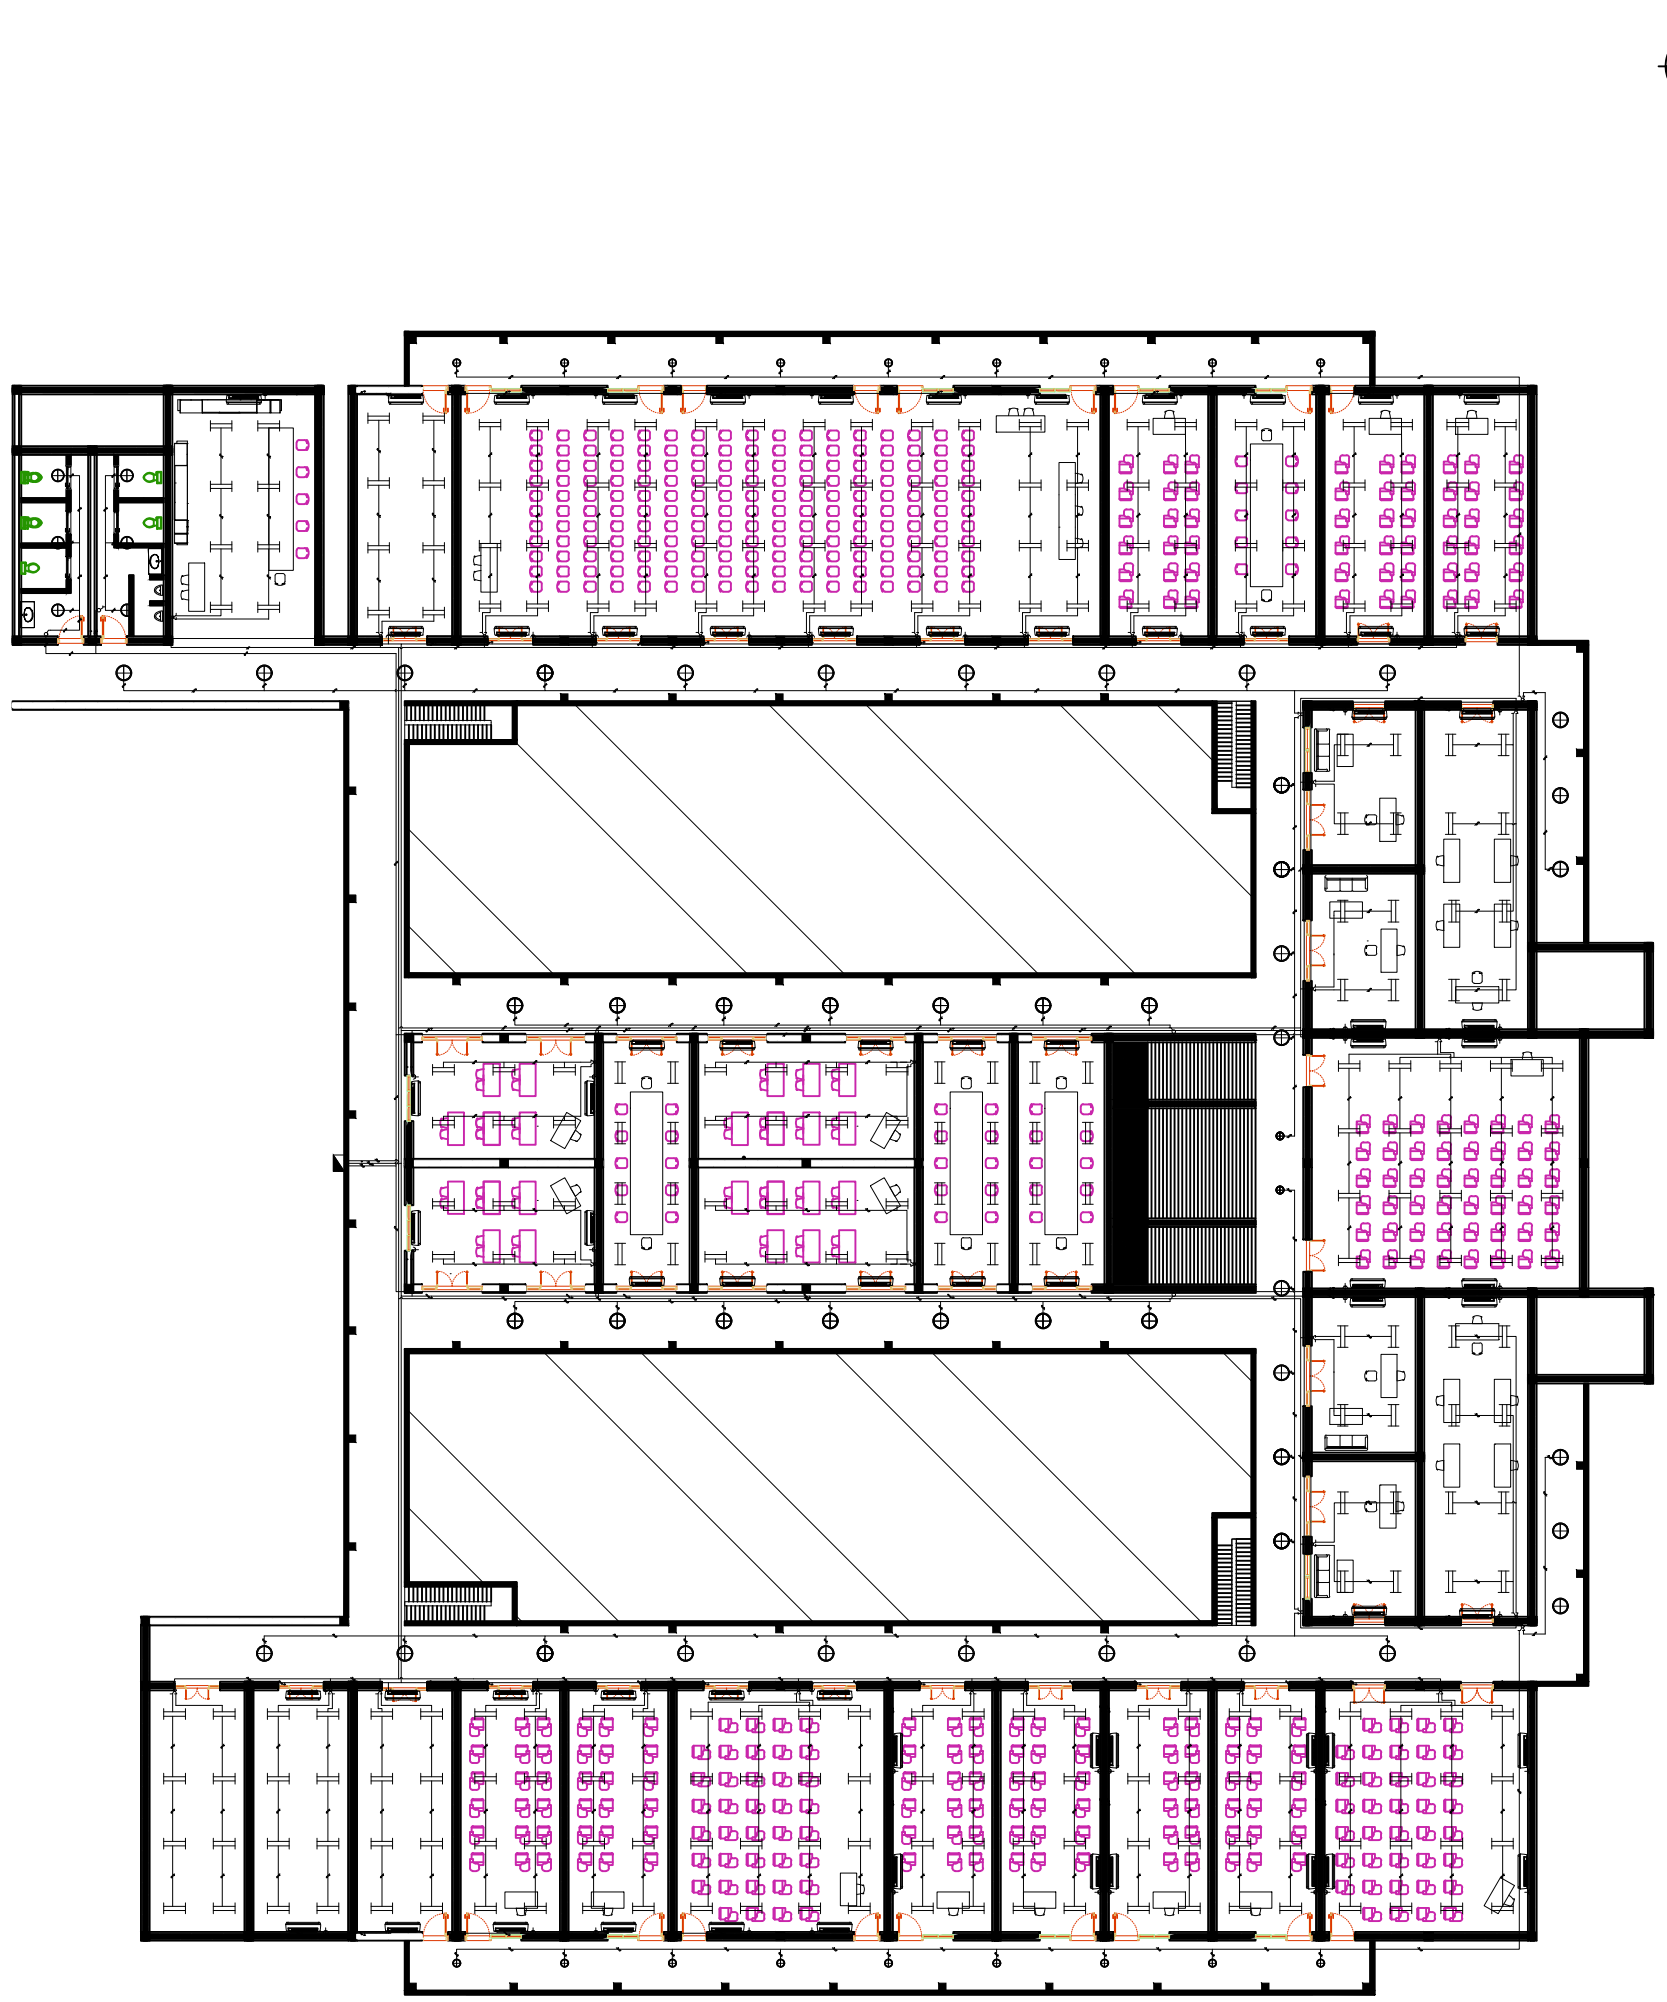

Project SLD Instalasi Listrik Gedung Herman Yohannes Lantai 2		Tanggal	24 Oktober 2024
		Digambar	Farrel Amaris Ipaenen Mirza Dyiaulhaq
		Dicek	Romy Dzaki Zharfan Hisyam Rifa'i Ma'ruf
Satuan: cm	Skala: 1:350	Ukuran Kertas	A3